



- | | | | |
|------|--|------|---|
| 1. | BOUNDARIES SHOWN FOR THE SITE (LOT 1 DP 23948) HAVE BEEN SOURCED FROM UNDERLYING SURVEY PLAN DP 23948, WHILST ADJACENT BOUNDARIES HAVE BEEN SOURCED FROM GRIP AND ARE SUBJECT TO SOME INACCURACIES. | 7. | THIS PLAN AND ITS CONTENTS SHOULD NOT BE USED FOR ANY REASON OTHER THAN ITS INTENDED PURPOSE. THIS PLAN AND SURVEYED INFORMATION DOES NOT INCLUDE ASSESSMENT OR REPRESENTATIONS CONCERNING: |
| 2. | THE UNDERLYING TITLE OT16A411 IS SUBJECT TO ENCUMBRANCES, REFER TO RECORD OF TITLE OT16A411 FOR DETAILS. SUBJECT EASEMENT FOR CONVEYING SEWAGE HAS BEEN SHOWN ON THE PLAN. | 7.1. | HAZARD REGISTERED, GROUND CONDITIONS, OR SUITABILITY FOR DEVELOPMENT. |
| 3. | EXISTING SERVICE ALIGNMENTS SHOWN HAVE BEEN SOURCED FROM CODOC GIS SERVICES. THIS IS NOT INTENDED TO BE A COMPLETE RECORD, BEFORE/BEHIND SERVICE SHOULD BE CONTACTED PRIOR TO UNDERTAKEN GROUND DISTURBING ACTIVITY. | 7.2. | THE IDENTITY, CORRECTNESS, OR USABILITY OF UTILITY SERVICES PORTALWAYS, OR SERVICE CONNECTIONS TO UTILITY NETWORKS. |
| 4. | INFORMATION WAS COLLECTED FROM SITE SURVEY CARRIED OUT 15/09/25. | 8. | THE USER OF THIS SURVEY INFORMATION SHOULD CONFIRM THE CORRECTNESS OF UTILITY SERVICES WITH UTILITY PROVIDERS AND SHOULD CONSULT THEM TO MARK OUT UNDERGROUND SERVICES ON THE GROUND PRIOR TO ANY CONSTRUCTION ON OR NEAR THE SITE. |
| 5. | CO-ORDINATES ARE IN TERMS OF NZGD2000 DATUM ON THE LINDIS CIRCUIT. HEIGHTS ARE IN TERMS OF NZVD16. | 9. | SPOT HEIGHTS AND OTHER HEIGHT LABELS HAVE NOT BEEN SHOWN ON THESE PLANS FOR PRESENTATION PURPOSES. REFERENCE SHOULD BE MADE TO THE DWG FILE TO VIEW THIS DATA. |
| 6. | ORIGIN MARK CO-ORDINATES: IT IV DP 471941 | 10. | AERIAL IMAGERY HAS BEEN SOURCED FROM LINZ DATA SERVICE (otago-02m-aerial-photos-2025). |
| 6.1. | E - 379195.974 | | |
| 6.2. | N - 767641.030 | | |
| 6.3. | H - 211.943 | | |

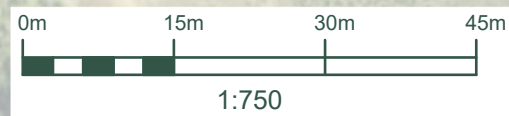

66°50'30"	64.32	LEGAL BOUNDARY (PRIMARY PARCEL)
_____	_____	LEGAL BOUNDARY (ADJACENT PARCEL)
125°09'00"	62.71	EASEMENT
== -350.0 ==		EXISTING CONTOURS (0.5m INTERVAL)
⚡ 24.12		SPOT HEIGHT LABEL
		BUILDING
—+—+—+—+—+—		BANK TOP / BOTTOM / BREAKLINE
—+—+—+—+—+—		WALL TOP / BOTTOM
—+—+—+—+—+—		FENCE
— — — — —		STORMWATER LINE (EXISTING)
— — — — —		WASTEWATER LINE (EXISTING)
— — — — —		WATERMAIN (EXISTING)
		MUD TANK / CLEANING EYE
		MARKER / CHAMBER
		WATER TOBY / VALVE / HYDRANT
		POWER BOX / TRANSFORMER
		TELECOM BOX / PIT
		STREETLIGHT / POWER POLE
		SIGN / POST
— . . —		FOOTPATH (LIMESTONE)
== — — — — —		CONCRETE / SEAL / ROAD CROWN
— — — — —		WATER LEVEL LINE
		SURVEY MARK

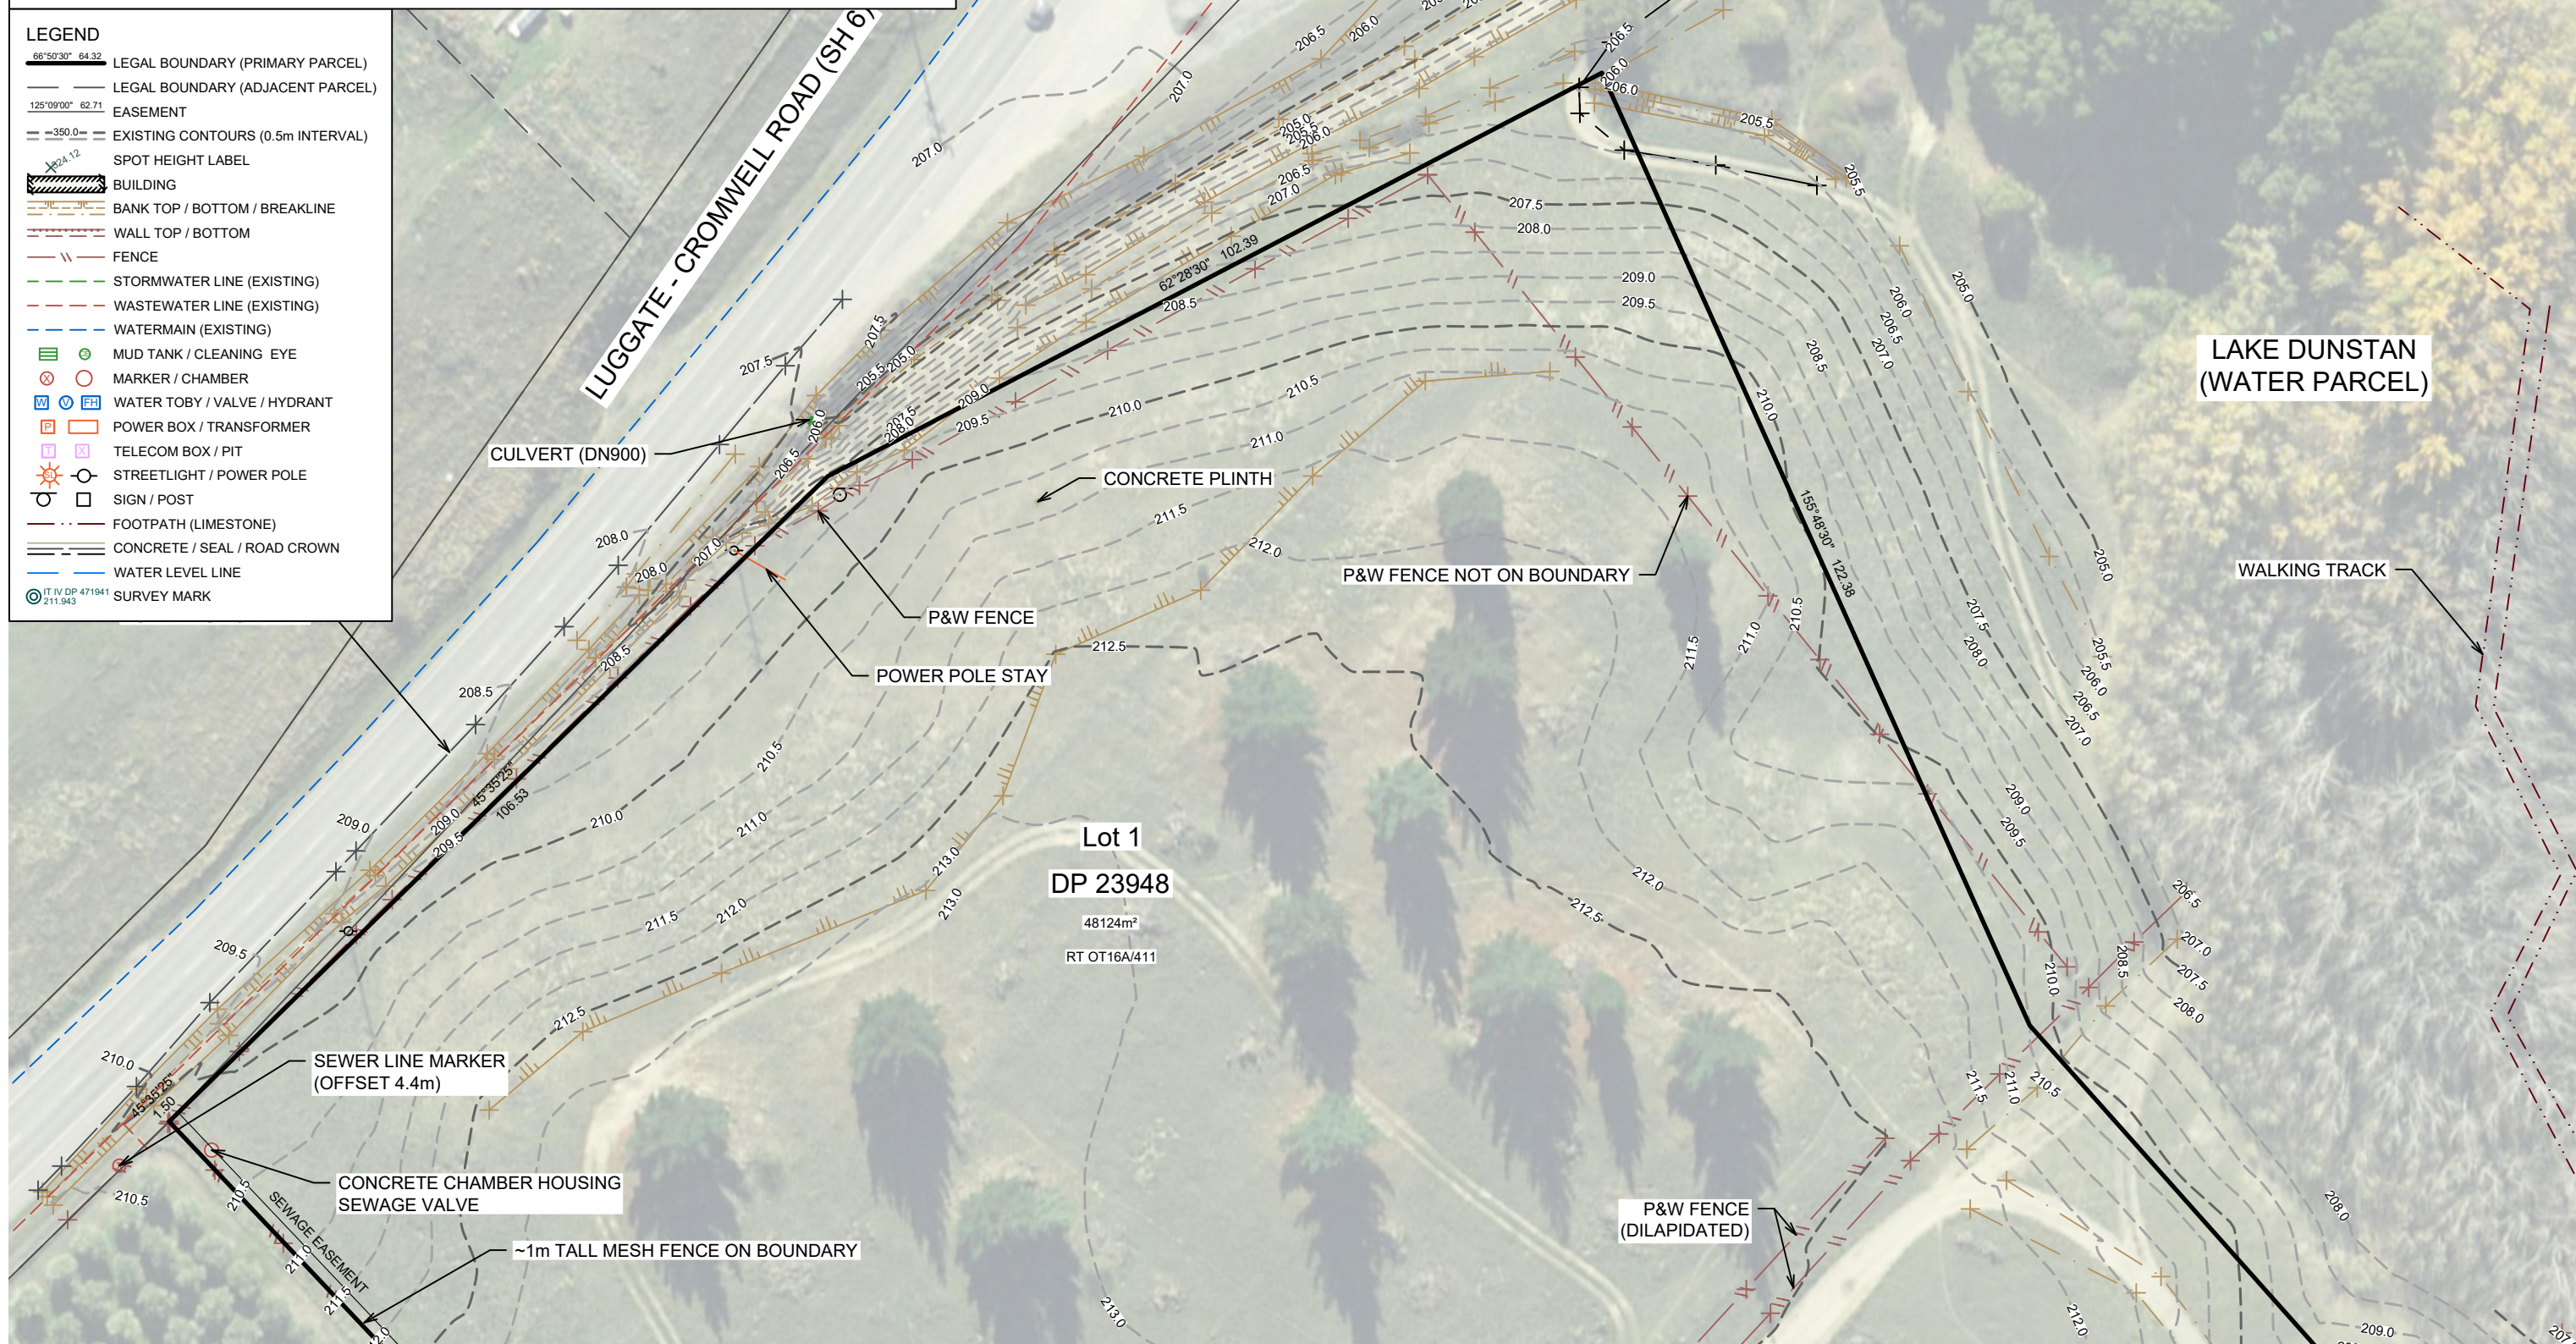

BRIAN DE GEEST
THELMA PLACE

DRAWING TITLE

**TOPOGRAPHIC SURVEY OF LOT 1 DP 23948
THELMA PLACE**

INSET DIAGRAM A

DATUM INFORMATION	
COORDINATE SYSTEM	NZGD2000
	LINDIS PEAK CIRCUIT
DATUM	NZVD2016
ORIGIN OF COORDINATES	IT IV DP 471941
ORIGIN OF LEVELS IT IV DP 471941	= RL:211.943

REV	DRAWN	DATE	NOTE
0	SJ	16.09.25	TOPOGRAPHIC SURVEY

STATUS FOR INFORMATION

SURVEYED	SJ	15.09.25
DESIGNED		
DRAWN	SJ	16.09.25
REVIEWED	WS	16.09.25
APPROVED		

© Paterson Pitts Limited Partnership

PROJECT	P240673
DRAWING NO	002
SHEET	111
REVISION	0
SCALE (A3)	1:750