


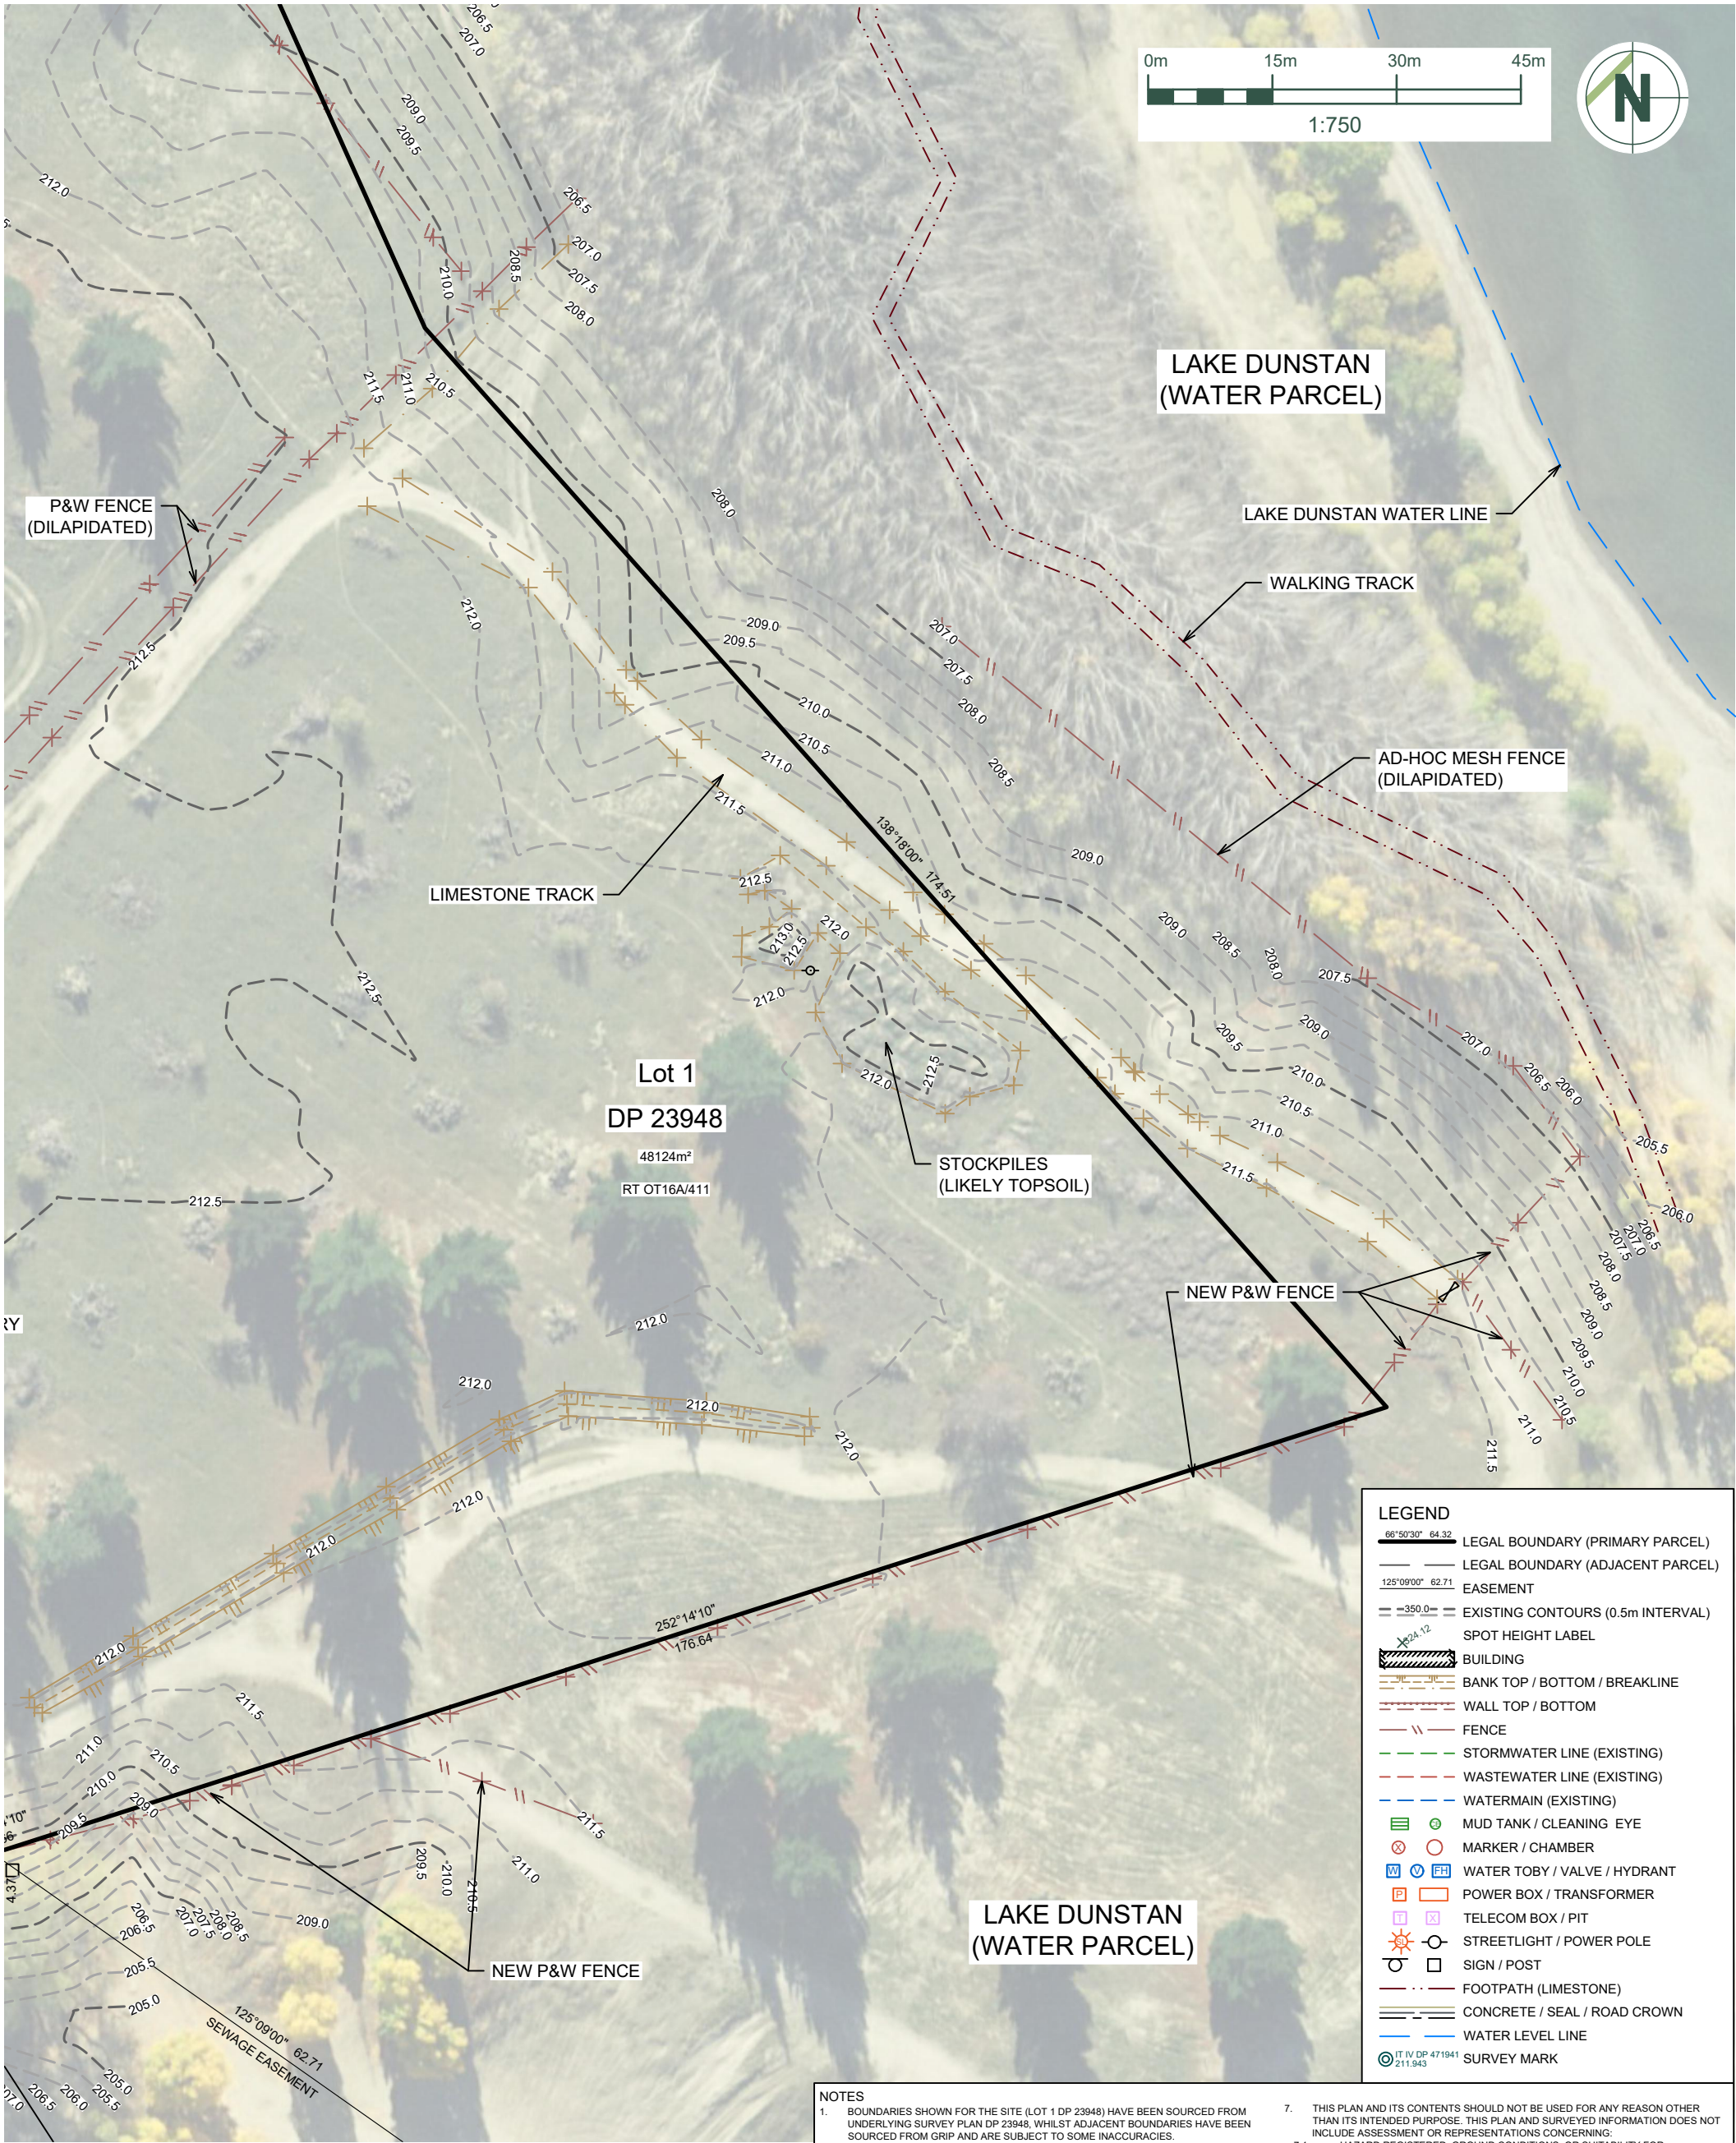

CLIENT
BRIAN DE GEEST
THEIMA PLACE

DRAWING TITLE
TOPOGRAPHIC SURVEY OF LOT 1 DP 23948
THEIMA PLACE

INSET DIAGRAM B

DATUM INFORMATION
COORDINATE SYSTEM
LINDIS PEAK CIRCUIT
NZGD2000
DATUM
NZVD2016
ORIGIN OF COORDINATES
IT IV DP 471941
ORIGIN OF LEVELS
IT IV DP 471941 = RL:211.943

NOTES

- BOUNDARIES SHOWN FOR THE SITE (LOT 1 DP 23948) HAVE BEEN SOURCED FROM UNDERLYING SURVEY PLAN DP 23948, WHILST ADJACENT BOUNDARIES HAVE BEEN SOURCED FROM GRIP AND ARE SUBJECT TO SOME INACCURACIES.
- THE UNDERLYING TITLE OT16A/411 IS SUBJECT TO ENCUMBRANCES, REFER TO RECORD OF TITLE OT16A/411 FOR DETAILS. SUBJECT EASEMENT FOR CONVEYING SEWAGE HAS BEEN SHOWN ON THE PLAN.
- EXISTING SERVICE ALIGNMENTS SHOWN HAVE BEEN SOURCED FROM CODC GIS SERVICES. THIS IS NOT INTENDED TO BE A COMPLETE RECORD, THE BEFOREDUG SERVICE SHOULD BE CONTACTED PRIOR TO UNDERTAKEN GROUND DISTURBING ACTIVITY.
- INFORMATION WAS COLLECTED FROM SITE SURVEY CARRIED OUT 15/09/25.
- CO-ORDINATES ARE IN TERMS OF NZGD2000 DATUM ON THE LINDIS CIRCUIT. HEIGHTS ARE IN TERMS OF NZVD2016.
- ORIGIN MARK CO-ORDINATES: IT IV DP 471941
6.1. E - 379195.974
6.2. N - 767641.030
6.3. H - 211.943
- THIS PLAN AND ITS CONTENTS SHOULD NOT BE USED FOR ANY REASON OTHER THAN ITS INTENDED PURPOSE. THIS PLAN AND SURVEYED INFORMATION DOES NOT INCLUDE ASSESSMENT OR REPRESENTATIONS CONCERNING:
7.1. HAZARD REGISTERED, GROUND CONDITIONS, OR SUITABILITY FOR DEVELOPMENT.
7.2. THE IDENTITY, CORRECTNESS, OR USABILITY OF UTILITY SERVICES PORTRAYED, OR SERVICE CONNECTIONS TO UTILITY NETWORKS.
- THE USER OF THIS SURVEY INFORMATION SHOULD CONFIRM THE CORRECTNESS OF UTILITY SERVICES WITH UTILITY PROVIDERS AND SHOULD CONSULT THEM TO MARK OUT UNDERGROUND SERVICES ON THE GROUND PRIOR TO ANY CONSTRUCTION ON OR NEAR THE SITE.
- SPOT HEIGHTS AND OTHER HEIGHT LABELS HAVE NOT BEEN SHOWN ON THESE PLANS FOR PRESENTATION PURPOSES. REFERENCE SHOULD BE MADE TO THE .DWG FILE TO VIEW THIS DATA.
- AERIAL IMAGERY HAS BEEN SOURCED FROM LINZ DATA SERVICE (otago-02m-rural-photos-2025).

REV	DRAWN	DATE	NOTE
0	SJ	16.09.25	TOPOGRAPHIC SURVEY

STATUS **FOR INFORMATION**

SURVEYED	SJ	15.09.25	PROJECT	P240673
DESIGNED			DRAWING NO	002
DRAWN	SJ	16.09.25	SHEET	112
REVIEWED	WS	16.09.25	REVISION	0
APPROVED			SCALE (A3)	1:750

© Paterson Pitts Limited Partnership