


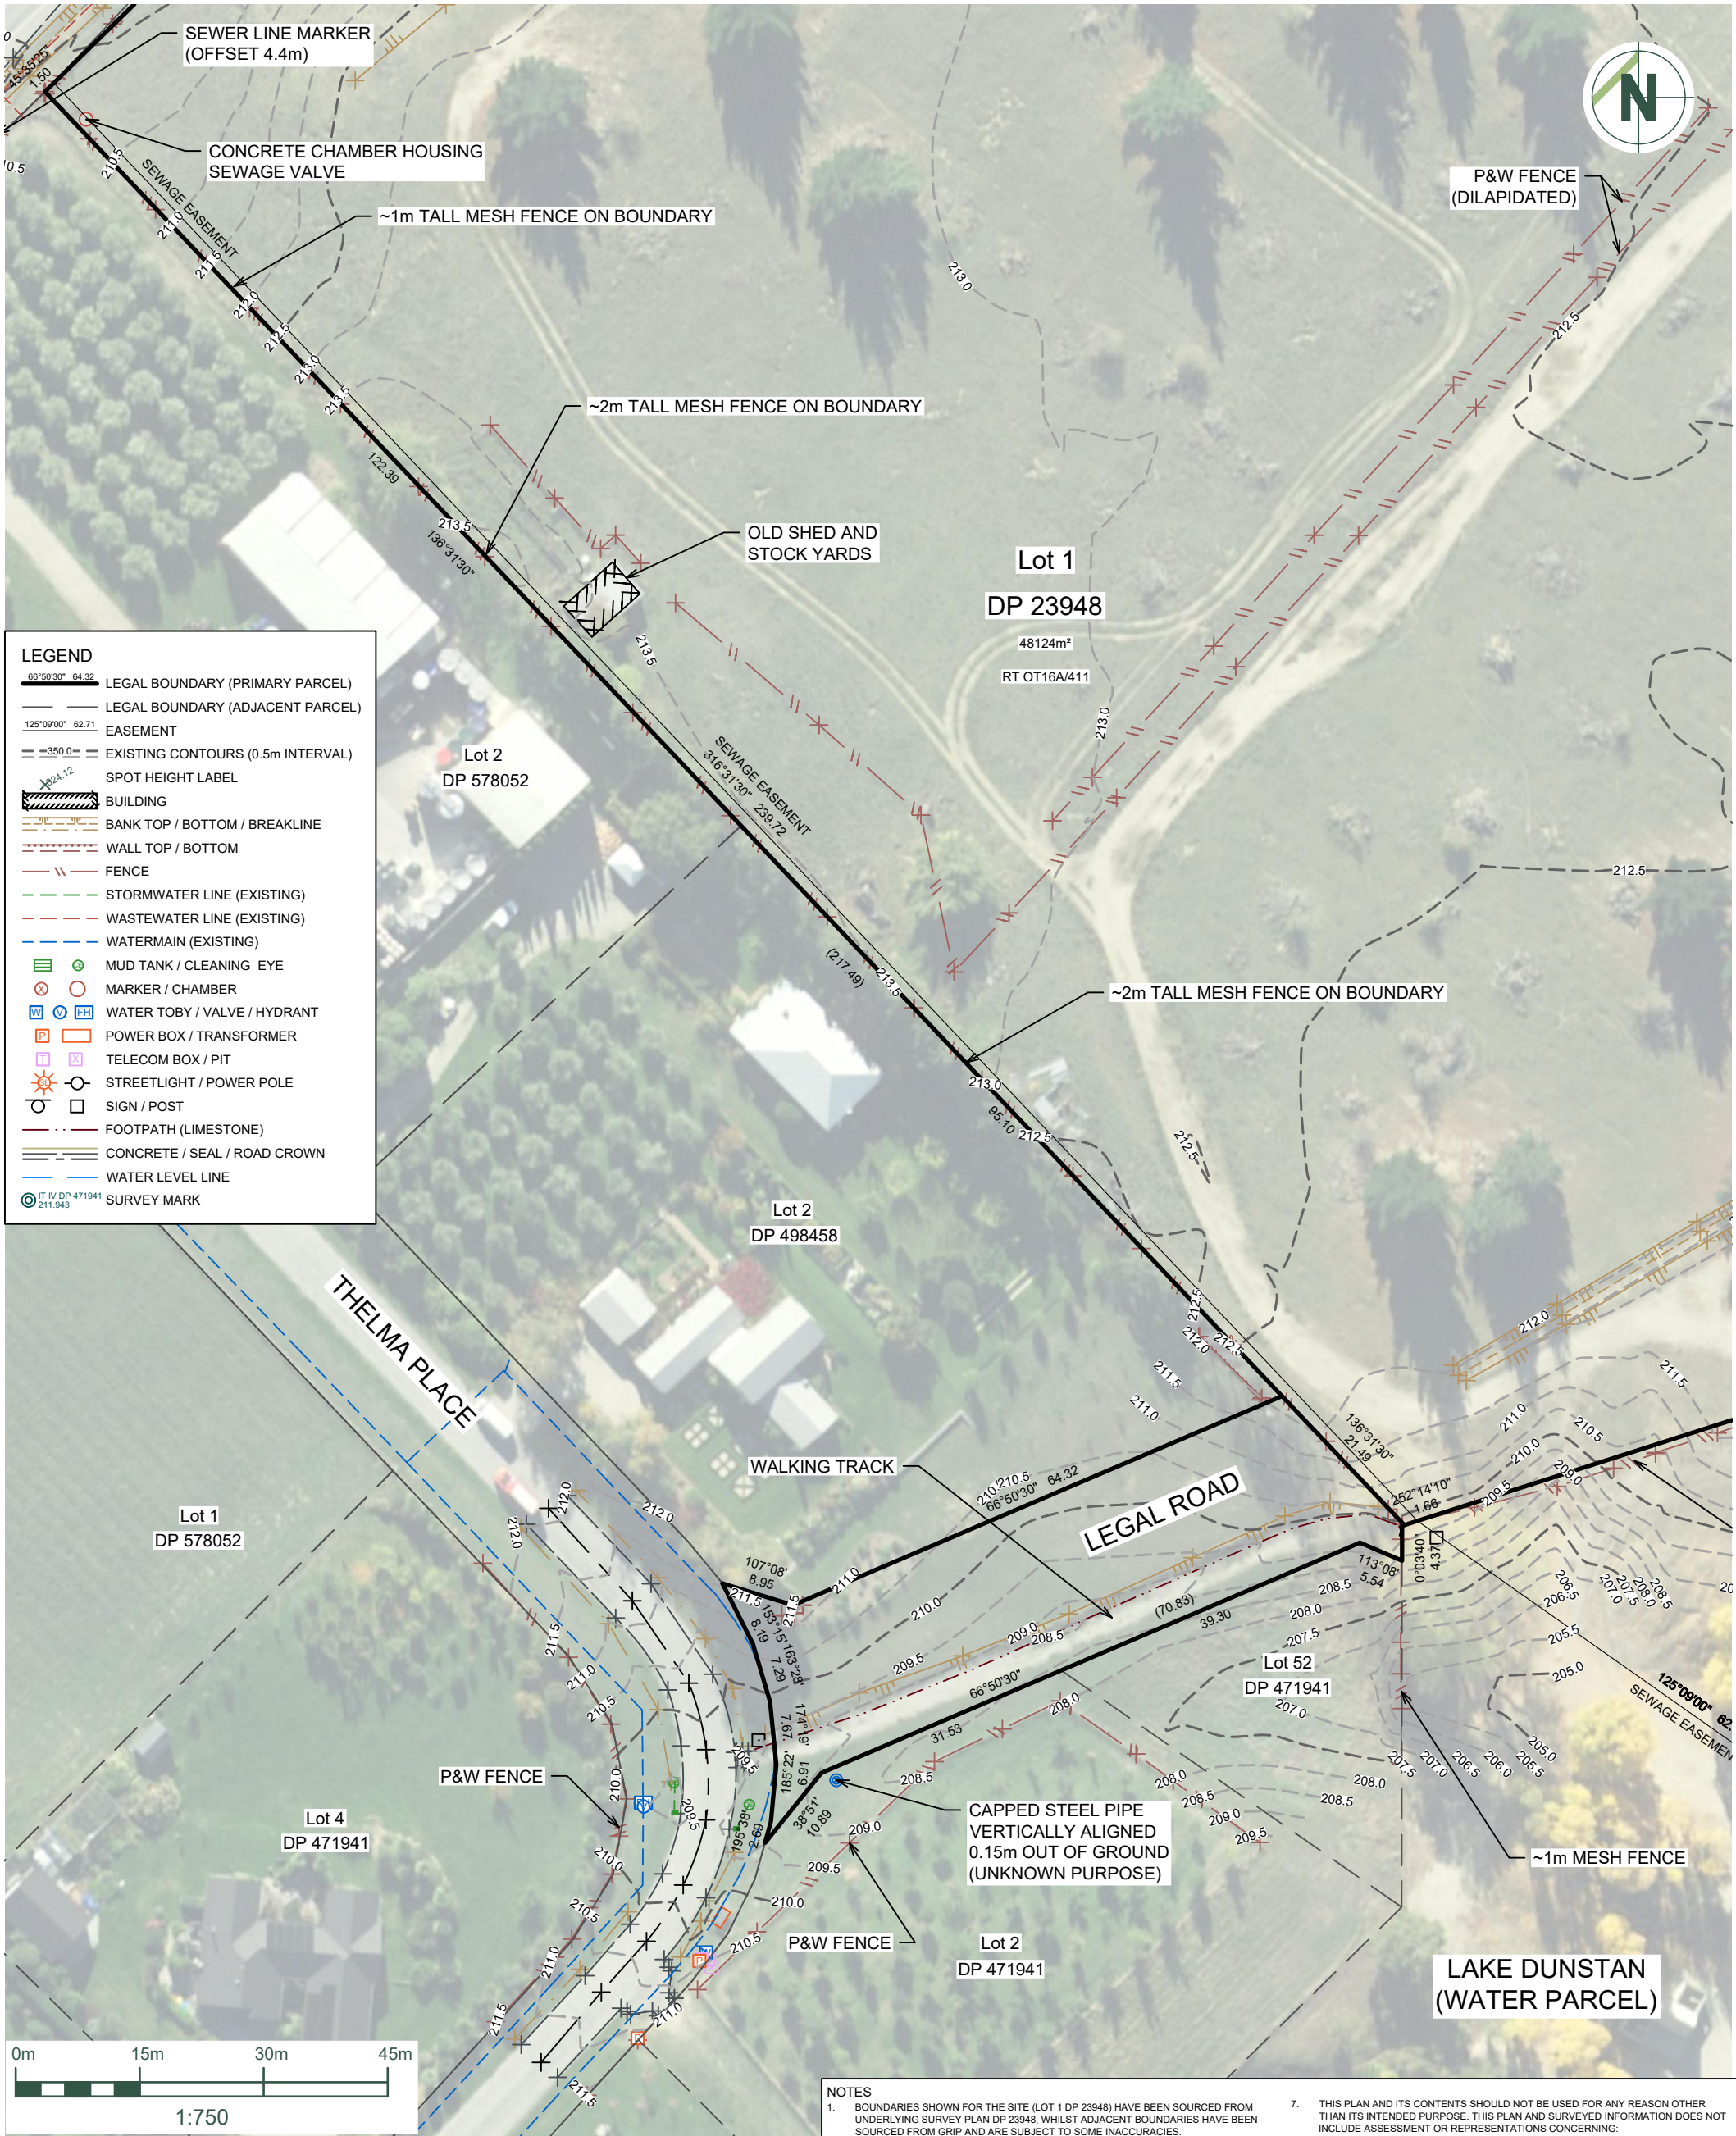

CLIENT
BRIAN DE GEEST
THELMA PLACE

DRAWING TITLE
TOPOGRAPHIC SURVEY OF LOT 1 DP 23948
THELMA PLACE

INSET DIAGRAM C

DATUM INFORMATION
COORDINATE SYSTEM
NZGD2000
LINDIS PEAK CIRCUIT
DATUM
NZVD2016
ORIGIN OF COORDINATES
IT IV DP 471941
ORIGIN OF LEVELS
IT IV DP 471941 = RL:211.943

REV DRAWN DATE NOTE
0 SJ 16.09.25 TOPOGRAPHIC SURVEY

STATUS **FOR INFORMATION**

SURVEYED SJ 15.09.25
DESIGNED
DRAWN SJ 16.09.25
REVIEWED WS 16.09.25
APPROVED

© Paterson Pitts Limited Partnership

PROJECT **P240673**
DRAWING NO **002**
SHEET **113**
REVISION **0**
SCALE (A3) **1:750**